


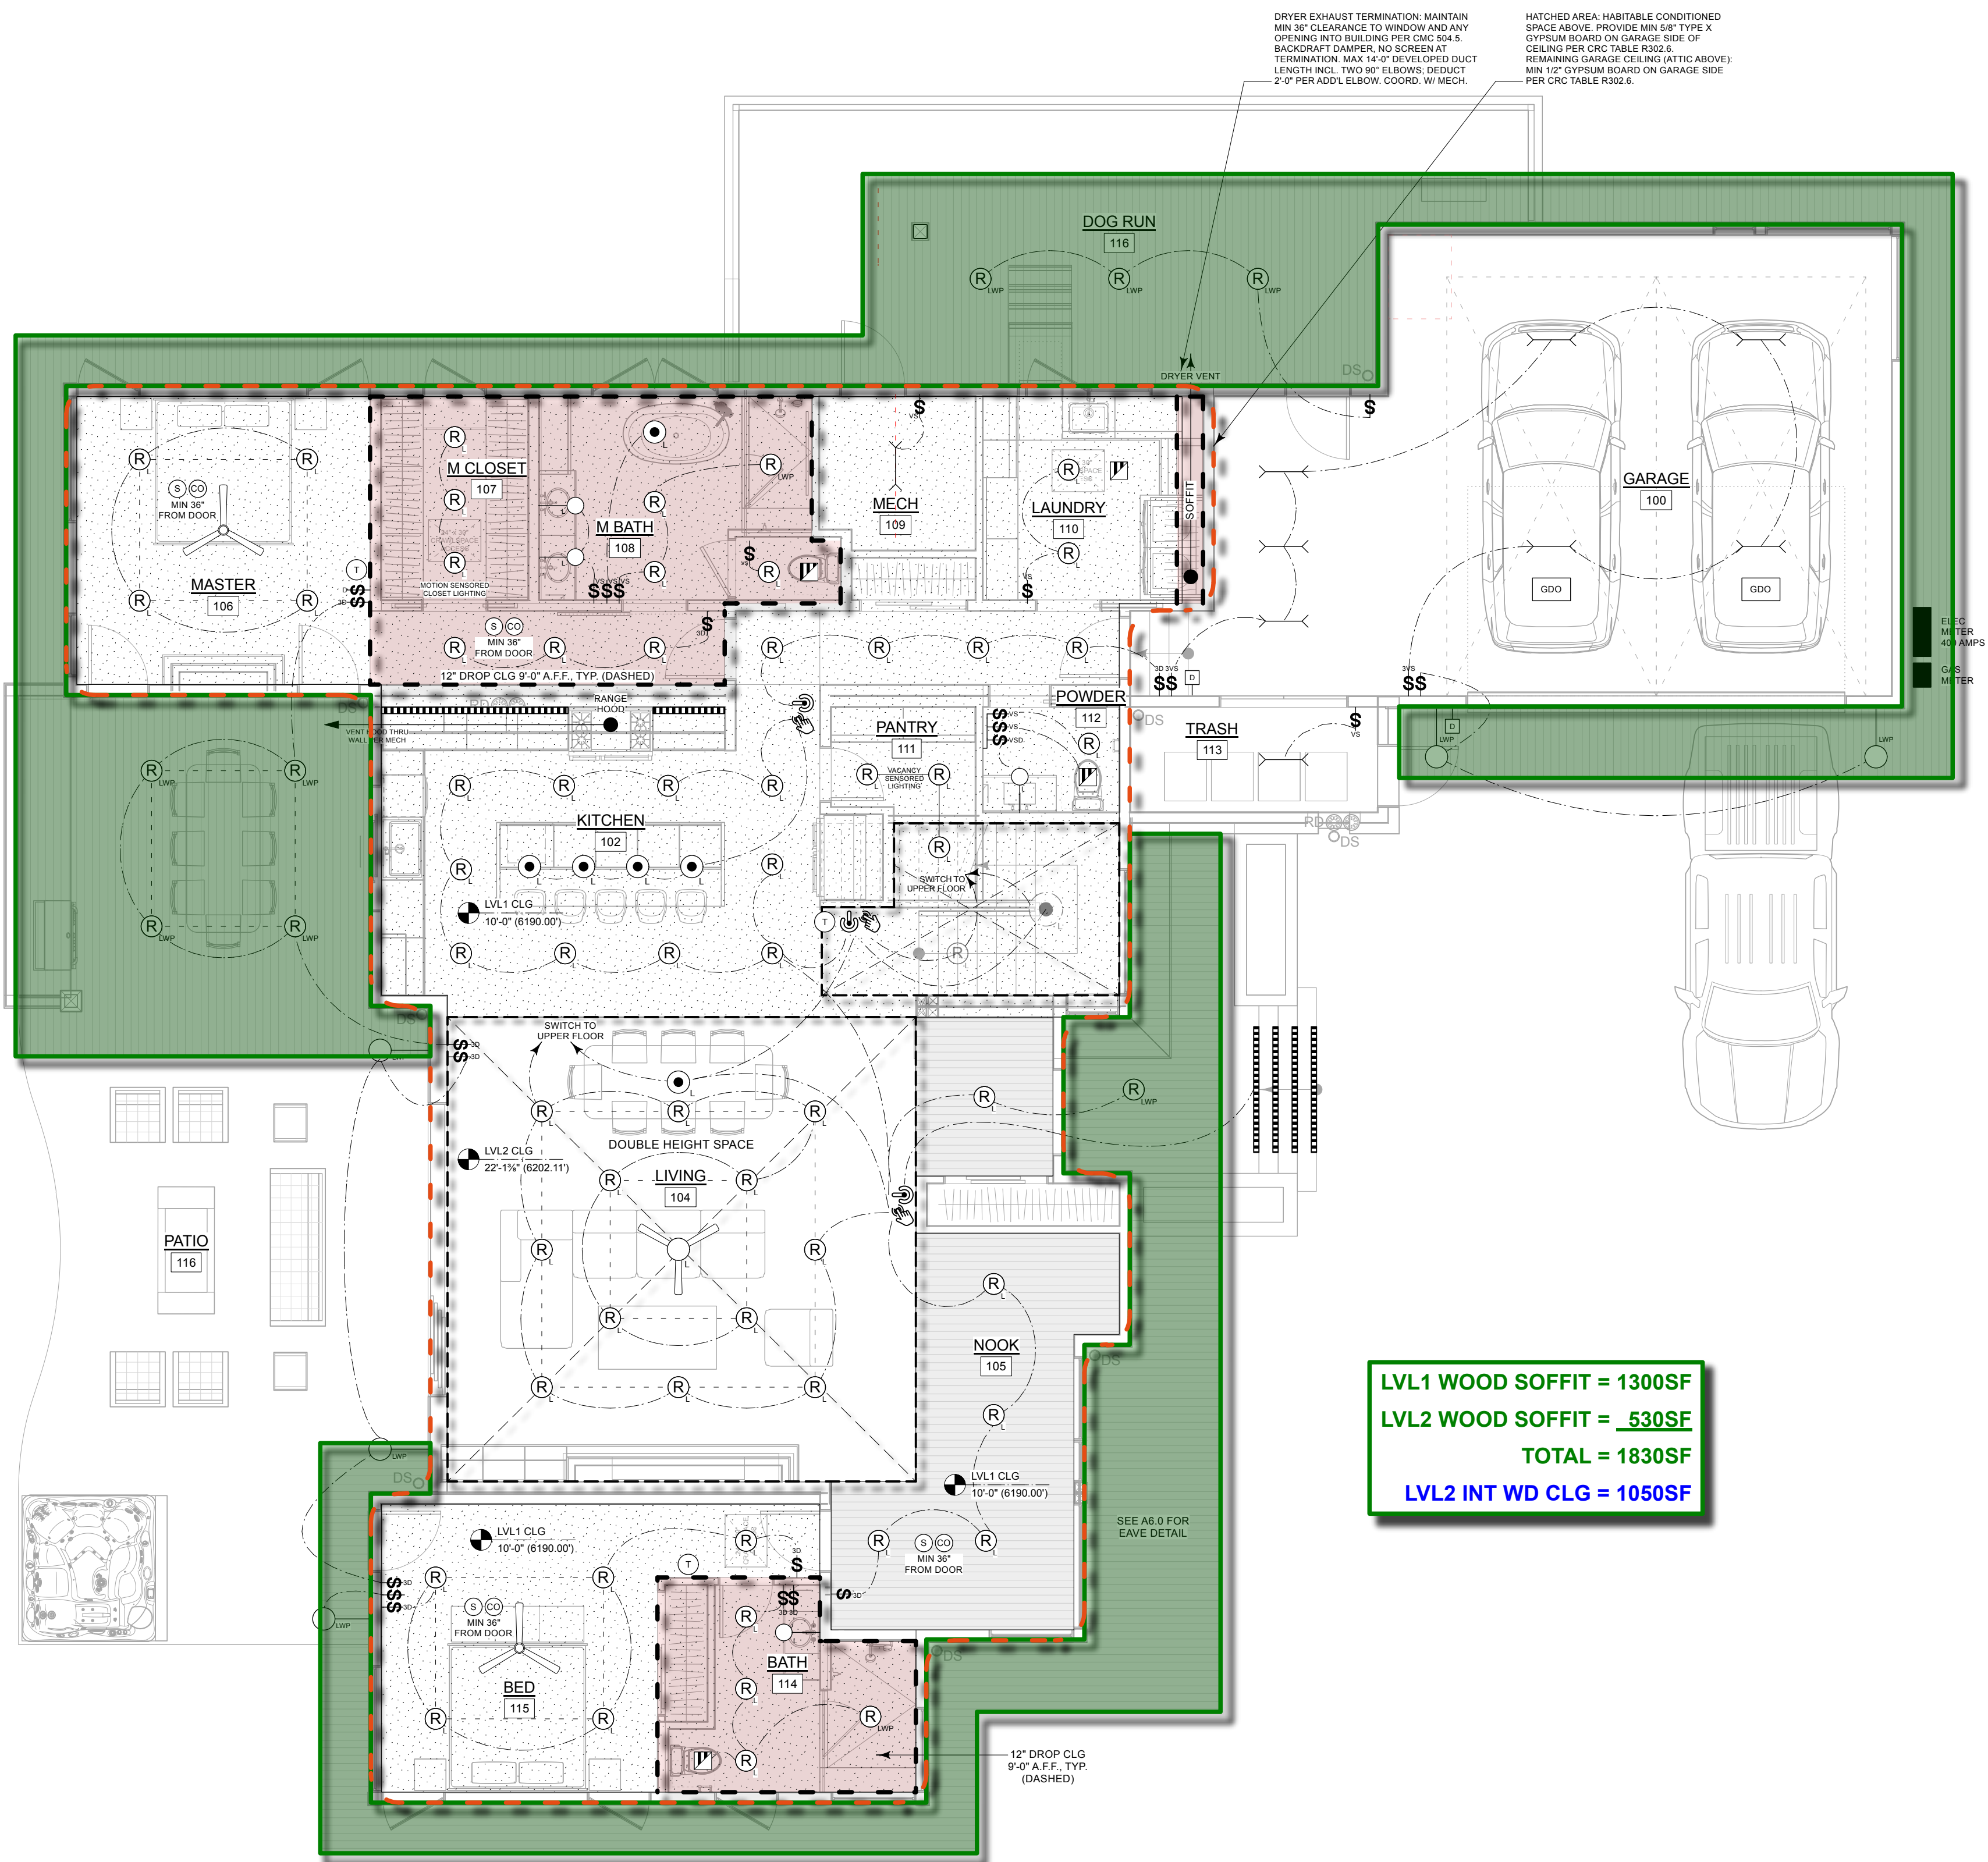


LEGEND

	DUPLEX RECEPTACLE		SMARTHOME LIGHTING CONTROLLER
	FOURPLEX RECEPTACLE		GARAGE DOOR DATA PAD
	WATERPROOF RECEPTACLE		DATA PORT/ WALL TELEPHONE OUTLET
	SWITCHED OUTLET		SINGLE POLE SWITCH
	GROUND FAULT CIRCUIT INTERRUPTER		DIMMER SWITCH
	DEDICATED OUTLET		THREE WAY SWITCH
	FLOOR OUTLET		VACANCY SENSOR SWITCH
	CEILING OUTLET		WEATHER PROOF SURFACE MOUNTED FIXTURE
	EXHAUST FAN, SEE MECH DWGS		WEATHER PROOF RECESSED DOWNLIGHT
	PENDANT		WEATHER PROOF WALL MOUNTED LIGHT
	SURFACE MOUNTED FIXTURE		GARAGE DOOR OPENER W/ LIGHT
	RECESSED LIGHT		SMOKE DETECTOR
	1' FIXTURE NOTE - LED LIGHT		CARBON MONOXIDE DETECTOR
	RECESSED DIRECTIONAL		THERMOSTAT
	WALL MOUNTED SCONCE		LED LIGHTING (CABINETS / EXT STAIRS)
	FLUORESCENT TUBE		GARBAGE DISPOSAL
	GAS LINE		HOSE BIB (FROST-FREE)

MECHANICAL / ELECTRICAL / LIGHTING NOTES (continued from A0.6)

- SECTION 49: GENERAL ELECTRICAL**
232. ALL ELECTRICAL WORK SHALL BE PERFORMED BY A LICENSED ELECTRICIAN.
233. THE ELECTRICAL CONTRACTOR SHALL GUARANTEE MATERIALS AND WORKMANSHIP AGAINST DEFECTS WHICH MAY OCCUR UNDER NORMAL USAGE FOR A PERIOD OF ONE (1) YEAR AFTER FINAL ACCEPTANCE. ALL GUARANTEE TIME PERIODS PROVIDED BY EQUIPMENT MANUFACTURERS SHALL CONTINUE TO BE IN EFFECT.
234. THE ELECTRICAL WORK SHALL INCLUDE THE SUPPLY AND INSTALLATION OF ALL ROUGH-IN MATERIALS, DEVICES, TRIM, AND SCHEDULED FIXTURES AS REQUIRED AND NECESSARY FOR ALL ELECTRICAL, TELEPHONE, APPLIANCES, AND EQUIPMENT, ETC.; UNO.
235. THE ELECTRICAL CONTRACTOR SHALL COORDINATE THE INSTALLATION OF THE MECHANICAL SYSTEMS WITH THE MECHANICAL CONTRACTOR TO INSURE ALL COMPONENTS OF EQUIPMENT AND CONTROLS ARE INCLUDED AND WIRED. ALL ELECTRICAL POWER WIRING, LOW VOLTAGE CONTROL WIRING, FUSES, CONDUIT, AND SWITCHES SHALL BE PROVIDED AND INSTALLED BY THE ELECTRICAL CONTRACTOR. THERMOSTATS SHALL BE PROVIDED AND INSTALLED BY THE MECHANICAL CONTRACTOR.
236. CUTTING, DRILLING, AND CHASING OF THE BUILDING SURFACES AS REQUIRED FOR SUPPORT ANCHORAGE, AND PASSAGE OF ELECTRICAL EQUIPMENT SHALL BE DONE BY THE ELECTRICAL CONTRACTOR. WHERE STRUCTURAL MEMBERS ARE INVOLVED, THE GENERAL CONTRACTOR'S APPROVAL SHALL BE FIRST OBTAINED.
237. THE ELECTRICAL CONTRACTOR SHALL ACCEPT FULL RESPONSIBILITY IN THE FORM OF PAYMENT TO THE GENERAL CONTRACTOR FOR COSTS INCURRED TO REPAIR, TO THE SATISFACTION OF THE OWNER, ANY COMPROMISING OF STRUCTURAL MEMBERS, WORK OF OTHER TRADES, FINISHES, OR OTHER DAMAGE CAUSED WHILE ON SITE AND PERFORMING ELECTRICAL WORK.
238. PROVIDE AND INSTALL A MINIMUM OF ONE SWITCHED LIGHT IN EACH ATTIC SPACE AND THREE SWITCHED LIGHTS IN THE UNDER FLOOR CRAWL SPACE; UNO.
239. ALL WORK PER 2025 CEC, MODULE WIRING FACTORY-INSTALLED UNDER STATE (HCD/ICC NTA) APPROVAL: GARAGE, EXTERIOR, SERVICE + SITE CONNECTIONS UNDER PLACER COUNTY PERMIT.
240. HABITABLE ROOMS: NO POINT ALONG THE FLOOR LINE OF ANY WALL SPACE 2 FT OR WIDER (INCL FIXED PANELS + ROOM DIVIDERS) MORE THAN 6 FT FROM A RECEPTACLE PER CEC 210.52(A).
241. MIN ONE WALL SWITCH-CONTROLLED LIGHTING OUTLET IN EACH HABITABLE ROOM, BATH, HALLWAY, STAIR, GARAGE + AT EXTERIOR ENTRANCES PER CEC 210.70(A).
242. GENERAL RECEPTACLES AT 12" AFF U.O.N. R328 AIP AREAS: RECEPTACLES MIN 15" AFF TO BOTTOM OF BOX; SWITCHES + CONTROLS MAX 48" AFF TO TOP OF BOX. SEE LIFE SAFETY + AIP SHEET.
243. BRANCH CIRCUIT, FEEDER + SERVICE CALC'S PER CEC ART 220; SMALL-APPLIANCE CIRCUITS AT 1,500 VA EACH PER 220.52(A).
244. MULTIWIRE BRANCH CIRCUITS: SIMULTANEOUS DISCONNECT OF ALL UNGROUNDED CONDUCTORS AT CIRCUIT ORIGIN PER CEC 210.4(B) + (D).
245. ALL 125V 15/20A RECEPTACLES IN AREAS PER CEC 210.52: LISTED TAMPER-RESISTANT PER CEC 408.12.
246. DEDICATED CIRCUITS FOR HEAT PUMP AIR HANDLERS, ERV, HPWH, DISPOSER, RANGE / OVEN, DISHWASHER + SIMILAR FIXED APPLIANCES PER CEC 210.11 + ART 422: VERIFY W/ MEQ EQUIPMENT SCHEDULES.
247. AFCI (COMBINATION TYPE) ON ALL 120V 15/20A CIRCUITS SERVING KITCHENS, LIVING / DINING / FAMILY ROOMS, DENS, BEDROOMS, SUNROOMS, REC ROOMS, CLOSETS, LAUNDRY, HALLWAYS + SIMILAR AREAS PER CEC 210.12(A).
248. GFCI: ALL KITCHEN COUNTERTOP RECEPTACLES PER 210.8(A)(6); ALL 125V 15/20A RECEPTACLES WITHIN 6 FT OF ANY SINK (INCL WET BAR) + LAUNDRY AREAS PER 210.8(A)(7) + (10); BATHROOMS PER 210.8(A)(1).
249. WALL COUNTERS 12" OR WIDER: RECEPTACLE SO NO POINT ALONG WALL EXCEEDS 24" FROM AN OUTLET PER 210.52(C)(1). COUNTERS SEPARATED BY RANGES, REFRIGERATORS OR SINKS ARE SEPARATE COUNTER SPACES.
250. ISLAND / PENINSULA RECEPTACLES PER 210.52(C)(2) + (3); COORDINATE POP-UP OR SIDE / END PANEL LOCATIONS W/ CASEWORK; NO FACE-UP RECEPTACLES.
251. COUNTERTOP RECEPTACLES MAX 20" ABOVE COUNTER; OUTLETS BLOCKED BY FIXED APPLIANCES DO NOT COUNT AS REQUIRED OUTLETS PER 210.52(C)(5).
252. BATHROOMS: MIN ONE RECEPTACLE WITHIN 3'-0" OF BASIN ON MIN ONE 20A CIRCUIT PER 210.52(D) + 210.11(C)(3).
253. KITCHEN / DINING / PANTRY / BREAKFAST: MIN TWO 20A SMALL-APPLIANCE CIRCUITS PER 210.11(C)(1); NO OTHER OUTLETS OR DIRECT-WIRED APPLIANCES ON THESE CIRCUITS.
254. LAUNDRY: MIN ONE RECEPTACLE ON SEPARATE 20A CIRCUIT WITHIN 6 FT OF APPLIANCE LOCATION PER 210.52(F) + 210.11(C)(2).
255. NO HANGING / PENDANT FIXTURE WITHIN 8 FT ABOVE OR 3 FT HORIZONTAL OF TUB RIM OR SHOWER THRESHOLD UNLESS LISTED WET / DAMP LOCATION PER CEC 410.10(D).
256. EXTERIOR LIGHTING: MANUAL SWITCH + MOTION SENSOR W/ PHOTOCONTROL, OR ASTRONOMICAL TIME CLOCK, W/ NO OVERRIDE OR BYPASS OF THE AUTOMATIC CONTROL, PER ENERGY CODE 190.0(K)(3).
257. LIGHTING HIGH-EFFICACY THROUGHOUT W/ DIMMER OR VACANCY SENSOR CONTROLS PER 150.0(K); RECESSED FIXTURES IN INSULATED CEILINGS IC-RATED + AIRTIGHT.
258. SMOKE (UL 217) + CO (UL 2034) ALARMS 120V HARDWIRED W/ BATTERY BACKUP; ALL INTERCONNECTED, PER 2025 CRC R310 / R311; FACTORY-INSTALLED UNDER HCD/NTA SCOPE; INTERCONNECT ACROSS MATE-LINES VERIFIED AT SET; LOCATIONS PER LIFE SAFETY + AIP SHEET.
259. EV CAPABLE PER CALGREEN 4.106.4.1: DEDICATED 208/240V BRANCH CIRCUIT RACEWAY TO GARAGE, BUSBAR CAPACITY + RESERVED BREAKER SPACE; PANEL + TERMINATION LABELED 'EV CAPABLE'.
260. PROVIDE PANEL CAPACITY, BREAKER SPACES + INTERCONNECTION PATHWAY FOR PV + BATTERY SCOPE PER T24 REPORT + ENERGY CODE 110.10; COORDINATE INVERTER / ESS LOCATIONS W/ ARCH + T24 DCOS.
261. BATH EXHAUST FANS ENERGY STAR W/ HUMIDITY CONTROL PER CALGREEN 4.508.1; SEE MECH FOR CFM + TERMINATIONS.
262. GARAGE DOOR OPENERS W/ BATTERY BACKUP PER HSC 19891.3; SEE WUI COMPLIANCE TABLE (CWUIC 504.9).
263. SEAL ELECTRICAL PENETRATIONS AT EXTERIOR ENVELOPE WEATHER-TIGHT; EXTERIOR DEVICES + FIXTURES LISTED FOR LOCATION; SEE WUI SHEET.
264. VERIFY APPLIANCE ELECTRICAL REQUIREMENTS W/ MFR SPECS + APPLIANCE SCHEDULE; REFERENCE ARCH PLANS; ALIGN SWITCH BOXES W/ RECEPTACLES BELOW WHERE POSSIBLE.

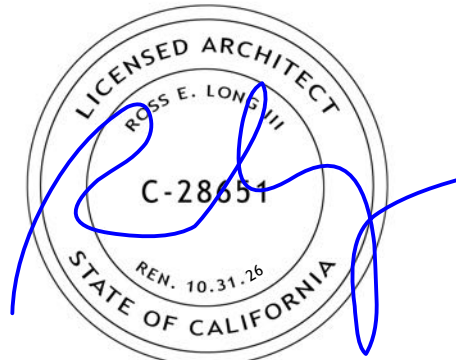

KELLY RESIDENCE
9095 HORNED LARK COURT
TRUCKEE, CA 96161
SCHAFFER'S MILL LOT 271
PLACER COUNTY APN: 107-190-009
OWNERS: SALLY & ROLAND KELLY

ISSUANCE	DATE
50% DESIGN SET	030926
100% DESIGN SET	040726
100% DESIGN SET V2	051826
PRELIMINARY DESIGN REVIEW	052826
50% STATE PERMIT SET	062126
FINAL DESIGN REVIEW	062926
100% PERMIT SET	080326
INTERIORS PRICING	081626

ARCHITECT



FACTORY



LEVEL 1 RCP / LIGHTING

THESE PLANS ARE CONSIDERED PRELIMINARY AND NOT FOR CONSTRUCTION UNLESS THEY BEAR THE ARCHITECT'S SEAL, AND CANNOT BE USED FOR ANY OTHER PURPOSE WITHOUT THE ARCHITECT'S WRITTEN PERMISSION. THESE PLANS ARE NOT TO BE REPRODUCED, CHANGED OR COPIED IN ANY FORM OR MANNER WITHOUT THE ARCHITECT'S WRITTEN PERMISSION.

scale
3/16"=1'-0"

sheet
A 2.4

© TONY LONG DESIGN 2026

PERMIT APPROVAL STAMP

GYPSUM BOARD FINISH @ ALL
CEILING. TYP. UNLESS
OTHERWISE NOTED.

ALL RESIDENTIAL LUMINAIRES
(INDOOR AND OUTDOOR) TO BE
HIGH-EFFICACY.

ALL LIGHTING FIXTURES AND
LOCATIONS TO BE CONFIRMED
WITH OWNER.



LVL1 WOOD SOFFIT = 1300SF
LVL2 WOOD SOFFIT = 530SF
TOTAL = 1830SF
LVL2 INT WD CLG = 1050SF


FACTORY-BUILT CONSTRUCTION SCOPE SHOWN IN
ORANGE SHADOWLINE ON ALL ARCH PLANS, TYP.

LEGEND

	DUPLUX RECEPTACLE		SMARTHOME LIGHTING CONTROLLER
	FOURPLEX RECEPTACLE ARC FAULT CIRCUIT INTERRUPTER		GARAGE DOOR DATA PAD
	WATERPROOF RECEPTACLE		DATA PORT/ WALL TELEPHONE OUTLET
	SWITCHED OUTLET		SINGLE POLE SWITCH
	GROUND FAULT CIRCUIT INTERRUPTER		DIMMER SWITCH
	DEDICATED OUTLET		THREE WAY SWITCH
	FLOOR OUTLET		VACANCY SENSOR SWITCH
	CEILING OUTLET		WEATHER PROOF SURFACE MOUNTED FIXTURE
	EXHAUST FAN, SEE MECH DWGS		WEATHER PROOF RECESSED DOWNLIGHT
	PENDANT		WEATHER PROOF WALL MOUNTED LIGHT
	SURFACE MOUNTED FIXTURE		GARAGE DOOR OPENER W/ LIGHT
	RECESSED LIGHT		SMOKE DETECTOR
	1' FIXTURE NOTE - LED LIGHT		CARBON MONOXIDE DETECTOR
	RECESSED DIRECTIONAL		THERMOSTAT
	WALL MOUNTED SCONCE		LED LIGHTING (CABINETS / EXT STAIRS)
	FLUORESCENT TUBE		GARBAGE DISPOSAL
	GAS LINE		HOSE BIB (FROST-FREE)

MECHANICAL / ELECTRICAL / LIGHTING NOTES (continued from A0.6)

- SECTION 49: GENERAL ELECTRICAL**
232. ALL ELECTRICAL WORK SHALL BE PERFORMED BY A LICENSED ELECTRICIAN.
233. THE ELECTRICAL CONTRACTOR SHALL GUARANTEE MATERIALS AND WORKMANSHIP AGAINST DEFECTS WHICH MAY OCCUR UNDER NORMAL USAGE FOR A PERIOD OF ONE (1) YEAR AFTER FINAL ACCEPTANCE. ALL GUARANTEE TIME PERIODS PROVIDED BY EQUIPMENT MANUFACTURERS SHALL CONTINUE TO BE IN EFFECT.
234. THE ELECTRICAL WORK SHALL INCLUDE THE SUPPLY AND INSTALLATION OF ALL ROUGH-IN MATERIALS, DEVICES, TRIM, AND SCHEDULED FIXTURES AS REQUIRED AND NECESSARY FOR ALL ELECTRICAL, TELEPHONE, APPLIANCES, AND EQUIPMENT, ETC.; UNO.
235. THE ELECTRICAL CONTRACTOR SHALL COORDINATE THE INSTALLATION OF THE MECHANICAL SYSTEMS WITH THE MECHANICAL CONTRACTOR TO INSURE ALL COMPONENTS OF EQUIPMENT AND CONTROLS ARE INCLUDED AND WIRED. ALL ELECTRICAL POWER WIRING, LOW VOLTAGE CONTROL WIRING, FUSES, CONDUIT, AND SWITCHES SHALL BE PROVIDED AND INSTALLED BY THE ELECTRICAL CONTRACTOR. THERMOSTATS SHALL BE PROVIDED AND INSTALLED BY THE MECHANICAL CONTRACTOR.
236. CUTTING, DRILLING, AND CHASING OF THE BUILDING SURFACES AS REQUIRED FOR SUPPORT ANCHORAGE, AND PASSAGE OF ELECTRICAL EQUIPMENT SHALL BE DONE BY THE ELECTRICAL CONTRACTOR. WHERE STRUCTURAL MEMBERS ARE INVOLVED, THE GENERAL CONTRACTOR'S APPROVAL SHALL BE FIRST OBTAINED.
237. THE ELECTRICAL CONTRACTOR SHALL ACCEPT FULL RESPONSIBILITY IN THE FORM OF PAYMENT TO THE GENERAL CONTRACTOR FOR COSTS INCURRED TO REPAIR, TO THE SATISFACTION OF THE OWNER, ANY COMPROMISING OF STRUCTURAL MEMBERS, WORK OF OTHER TRADES, FINISHES, OR OTHER DAMAGE CAUSED WHILE ON SITE AND PERFORMING ELECTRICAL WORK.
238. PROVIDE AND INSTALL A MINIMUM OF ONE SWITCHED LIGHT IN EACH ATTIC SPACE AND THREE SWITCHED LIGHTS IN THE UNDER FLOOR CRAWL SPACE; UNO.
239. ALL WORK PER 2025 CEC, MODULE WIRING FACTORY-INSTALLED UNDER STATE (HCD/ICC NTA) APPROVAL; GARAGE, EXTERIOR, SERVICE + SITE CONNECTIONS UNDER PLACER COUNTY PERMIT.
240. HABITABLE ROOMS: NO POINT ALONG THE FLOOR LINE OF ANY WALL SPACE 2 FT OR WIDER (INCL FIXED PANELS + ROOM DIVIDERS) MORE THAN 6 FT FROM A RECEPTACLE PER CEC 210.52(A).
241. MIN ONE WALL SWITCH-CONTROLLED LIGHTING OUTLET IN EACH HABITABLE ROOM, BATH, HALLWAY, STAIR, GARAGE + AT EXTERIOR ENTRANCES PER CEC 210.70(A).
242. GENERAL RECEPTACLES AT 12" AFF U.O.N. R328 AIP AREAS: RECEPTACLES MIN 15" AFF TO BOTTOM OF BOX; SWITCHES + CONTROLS MAX 48" AFF TO TOP OF BOX. SEE LIFE SAFETY + AIP SHEET.
243. BRANCH CIRCUIT, FEEDER + SERVICE CALC'S PER CEC ART 220; SMALL-APPLIANCE CIRCUITS AT 1,500 VA EACH PER 220.52(A).
244. MULTIWIRE BRANCH CIRCUITS: SIMULTANEOUS DISCONNECT OF ALL UNGROUNDED CONDUCTORS AT CIRCUIT ORIGIN PER CEC 210.4(B) + (D).
245. ALL 125V 15/20A RECEPTACLES IN AREAS PER CEC 210.52: LISTED TAMPER-RESISTANT PER CEC 408.12.
246. DEDICATED CIRCUITS FOR HEAT PUMP AIR HANDLERS, ERV, HPWH, DISPOSER, RANGE / OVEN, DISHWASHER + SIMILAR FIXED APPLIANCES PER CEC 210.11 + ART 422; VERIFY W/ MEG EQUIPMENT SCHEDULES.
247. AFCI (COMBINATION TYPE) ON ALL 120V 15/20A CIRCUITS SERVING KITCHENS, LIVING / DINING / FAMILY ROOMS, DENS, BEDROOMS, SUNROOMS, REC ROOMS, CLOSETS, LAUNDRY, HALLWAYS + SIMILAR AREAS PER CEC 210.12(A).
248. GFCI: ALL KITCHEN COUNTERTOP RECEPTACLES PER 210.8(A)(6); ALL 125V 15/20A RECEPTACLES WITHIN 6 FT OF ANY SINK (INCL WET BAR) + LAUNDRY AREAS PER 210.8(A)(7) + (10); BATHROOMS PER 210.8(A)(1).
249. WALL COUNTERS 12" OR WIDER: RECEPTACLE SO NO POINT ALONG WALL EXCEEDS 24" FROM AN OUTLET PER 210.52(C)(1). COUNTERS SEPARATED BY RANGES, REFRIGERATORS OR SINKS ARE SEPARATE COUNTER SPACES.
250. ISLAND / PENINSULA RECEPTACLES PER 210.52(C)(2) + (3); COORDINATE POP-UP OR SIDE / END PANEL LOCATIONS W/ CASEWORK; NO FACE-UP RECEPTACLES.
251. COUNTERTOP RECEPTACLES MAX 20" ABOVE COUNTER; OUTLETS BLOCKED BY FIXED APPLIANCES DO NOT COUNT AS REQUIRED OUTLETS PER 210.52(C)(5).
252. BATHROOMS: MIN ONE RECEPTACLE WITHIN 3'-0" OF BASIN ON MIN ONE 20A CIRCUIT PER 210.52(D) + 210.11(C)(3).
253. KITCHEN / DINING / PANTRY / BREAKFAST: MIN TWO 20A SMALL-APPLIANCE CIRCUITS PER 210.11(C)(1); NO OTHER OUTLETS OR DIRECT-WIRED APPLIANCES ON THESE CIRCUITS.
254. LAUNDRY: MIN ONE RECEPTACLE ON SEPARATE 20A CIRCUIT WITHIN 6 FT OF APPLIANCE LOCATION PER 210.52(F) + 210.11(C)(2).
255. NO HANGING / PENDANT FIXTURE WITHIN 8 FT ABOVE OR 3 FT HORIZONTAL OF TUB RIM OR SHOWER THRESHOLD UNLESS LISTED WET / DAMP LOCATION PER CEC 410.10(D).
256. EXTERIOR LIGHTING: MANUAL SWITCH + MOTION SENSOR W/ PHOTOCONTROL, OR ASTRONOMICAL TIME CLOCK, W/ NO OVERRIDE OR BYPASS OF THE AUTOMATIC CONTROL, PER ENERGY CODE 190.0(K)(3).
257. LIGHTING HIGH-EFFICACY THROUGHOUT W/ DIMMER OR VACANCY SENSOR CONTROLS PER 190.0(K); RECESSED FIXTURES IN INSULATED CEILINGS IC-RATED + AIRTIGHT.
258. SMOKE (UL 217) + CO (UL 2034) ALARMS 120V HARDWIRED W/ BATTERY BACKUP; ALL INTERCONNECTED, PER 2025 CRC R310 / R311; FACTORY-INSTALLED UNDER HCD/NTA SCOPE; INTERCONNECT ACROSS MATE-LINES VERIFIED AT SET; LOCATIONS PER LIFE SAFETY + AIP SHEET.
259. EV CAPABLE PER CALGREEN 4.106.4.1; DEDICATED 208/240V BRANCH CIRCUIT RACEWAY TO GARAGE, BUSBAR CAPACITY + RESERVED BREAKER SPACE; PANEL + TERMINATION LABELED 'EV CAPABLE'.
260. PROVIDE PANEL CAPACITY, BREAKER SPACES + INTERCONNECTION PATHWAY FOR PV + BATTERY SCOPE PER T24 REPORT + ENERGY CODE 110.10; COORDINATE INVERTER / ESS LOCATIONS W/ ARCH + T24 DCOS.
261. BATH EXHAUST FANS ENERGY STAR W/ HUMIDITY CONTROL PER CALGREEN 4.508.1; SEE MECH FOR CFM + TERMINATIONS.
262. GARAGE DOOR OPENERS W/ BATTERY BACKUP PER HSC 19891.3; SEE WUI COMPLIANCE TABLE (CWUIC 504.9).
263. SEAL ELECTRICAL PENETRATIONS AT EXTERIOR ENVELOPE WEATHER-TIGHT; EXTERIOR DEVICES + FIXTURES LISTED FOR LOCATION; SEE WUI SHEET.
264. VERIFY APPLIANCE ELECTRICAL REQUIREMENTS W/ MFR SPECS + APPLIANCE SCHEDULE; REFERENCE ARCH PLANS; ALIGN SWITCH BOXES W/ RECEPTACLES BELOW WHERE POSSIBLE.

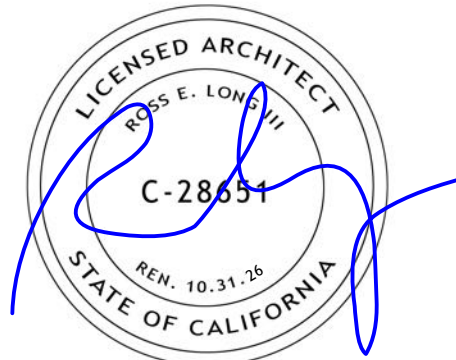

KELLY RESIDENCE
9095 HORNED LARK COURT
TRUCKEE, CA 96161
SCHAFER'S MILL LOT 271
PLACER COUNTY APN: 107-190-009
OWNERS: SALLY & ROLAND KELLY

ISSUANCE	DATE
50% DESIGN SET	030926
100% DESIGN SET	040726
100% DESIGN SET V2	051826
PRELIMINARY DESIGN REVIEW	052826
50% STATE PERMIT SET	062126
FINAL DESIGN REVIEW	062926
100% PERMIT SET	080326
INTERIORS PRICING	081626

ARCHITECT



FACTORY



LEVEL 2 RCP /
LIGHTING

THESE PLANS ARE CONSIDERED PRELIMINARY AND NOT FOR
CONSTRUCTION UNLESS THEY BEAR THE ARCHITECT'S SEAL,
STAMP, AND SIGNATURE. THEY EXPRESS THE ARCHITECT'S
LAW COPYRIGHT AND OTHER PROPER RIGHTS TO ALL
DESIGNS AND INFORMATION IN THESE PLANS. THESE PLANS ARE
NOT TO BE REPRODUCED, CHANGED OR COPIED IN ANY FORM
OR MANNER WITHOUT THE WRITTEN PERMISSION OF THE ARCHITECT.

scale
3/16"=1'-0"

sheet
A 2.6

© TONY LONG DESIGN 2026

PERMIT APPROVAL STAMP